


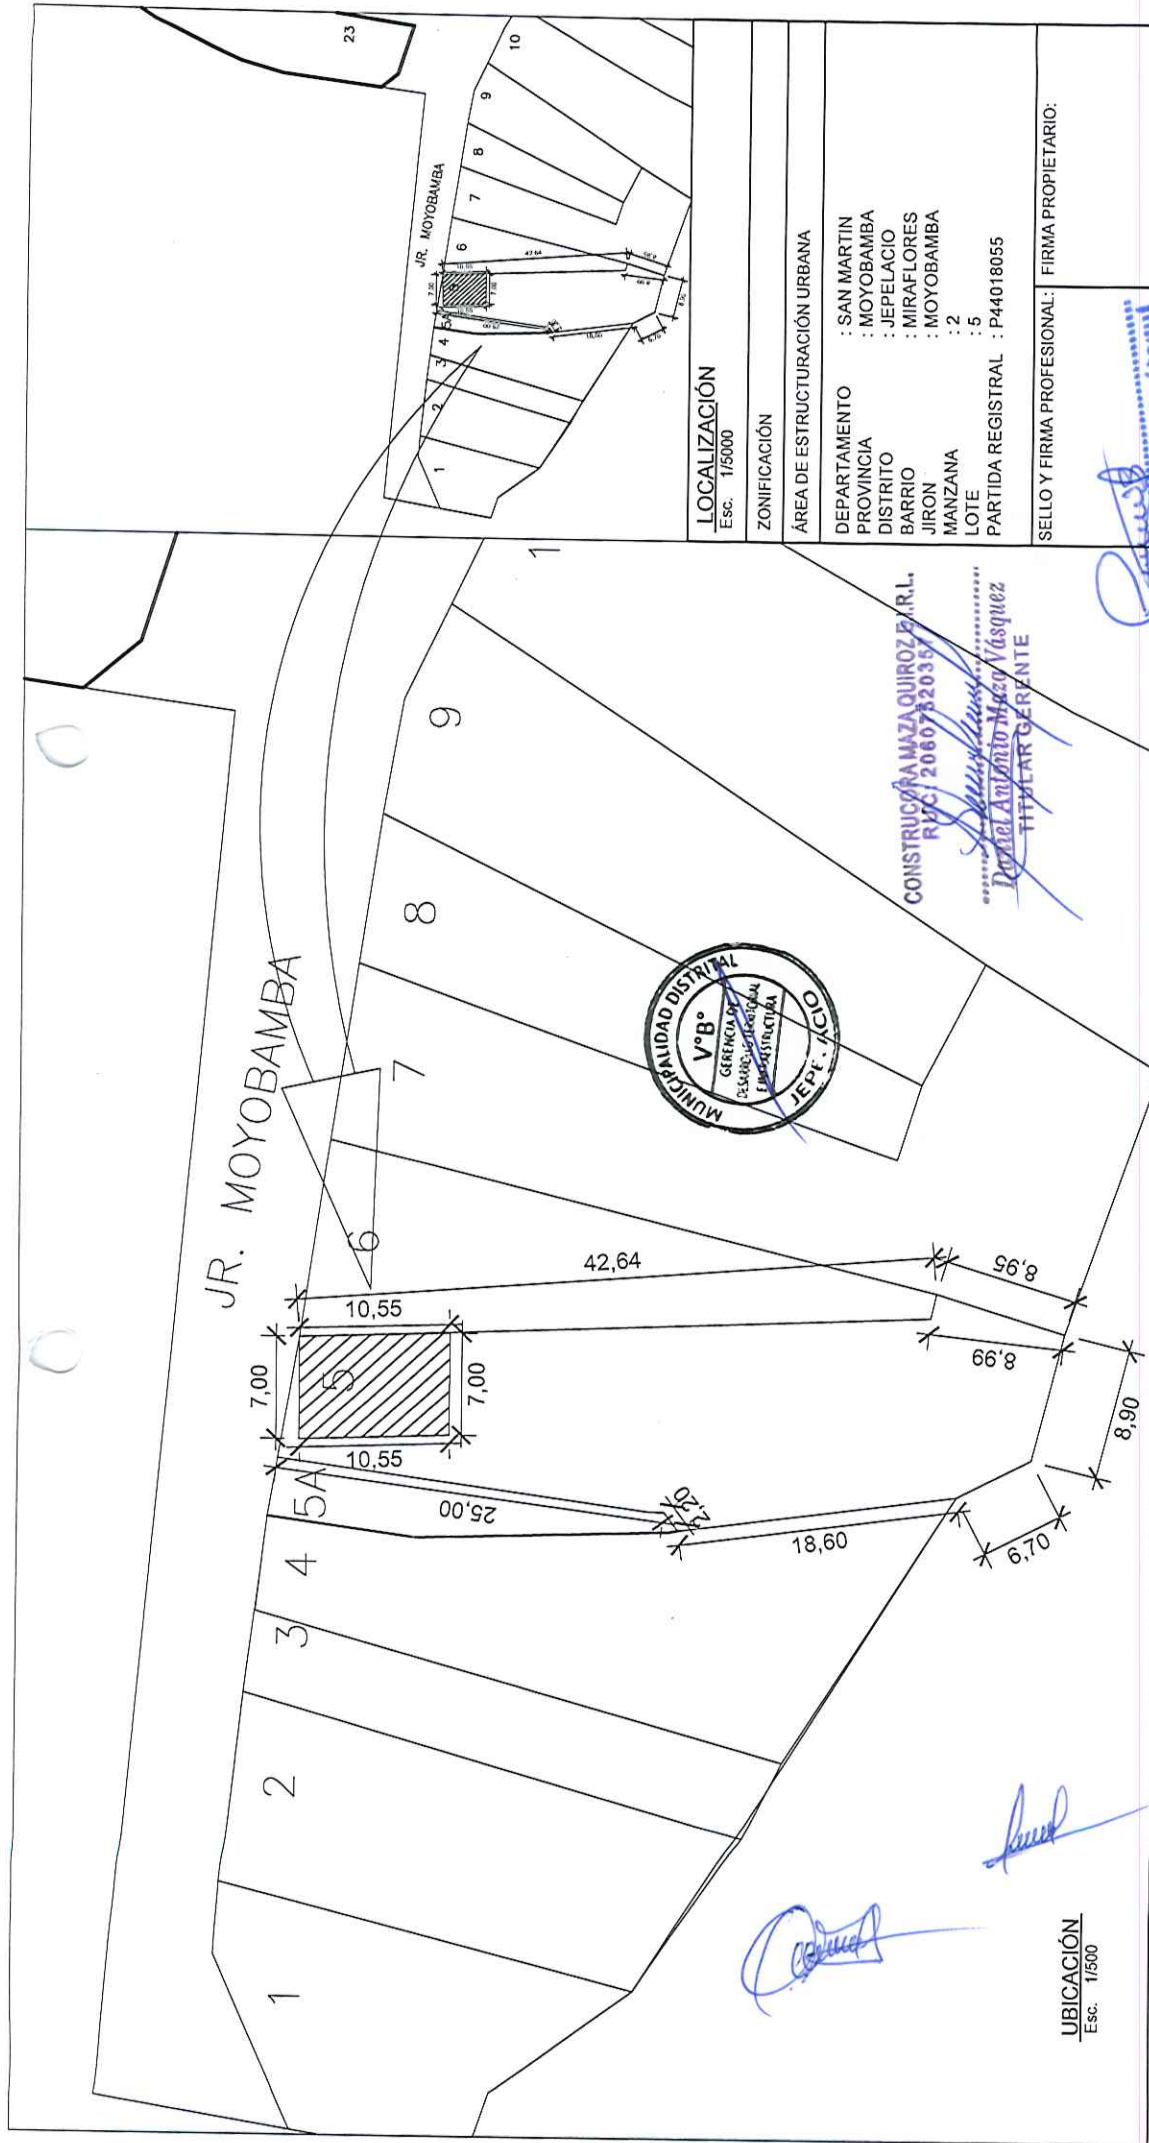

LOCALIZACIÓN
Esc. 1/5000

ZONIFICACIÓN

ÁREA DE ESTRUCTURACIÓN URBANA

DEPARTAMENTO : SAN MARTIN
PROVINCIA : MOYOBAMBA
DISTRITO : JEPELACIO
BARRIO : MIRAFLORES
JIRON : MOYOBAMBA
MANZANA : 2
LOTE : 5
PARTIDA REGISTRAL : P44018055

SELO Y FIRMA PROFESIONAL: FIRMA PROPIETARIO:

DANIEL SUAREZ CALDERON

PROYECTO: VIVIENDA UNIFAMILIAR

PLANO: UBICACION Y LOCALIZACION

LAMINA: U-01

ESCALA: 1 / 500
1 / 5000
FECHA: ABRIL, 2024


CUADRO DE AREAS (m2)

PARAMETROS	NORMATIVO	PROYECTO	Nº DE PISOS	AREAS DECLARADAS			TOTAL
				DEMOLICIÓN	NUOVA	AMP./REM.	
USOS	Comercial, residencial y otros señalados en el PDU	VIVIENDA UNIFAMILIAR	UN PISO		73.85 m2		
DENSIDAD NETA	100 a 660 Hab. / ha	NO APLICA					
COEFICIENTE EDIFICACIÓN	1.2 Unifilar - 1.8 Multifamiliar	0.14					
% AREA LIBRE	30 % Vivienda, uso Comercial no exigible	(00.86) %					
ALTURA MÁXIMA	02 Pisos, (6.40 ml) + Azotea	UN PISO					
RETIRO MÍNIMO	--	--					
POSTERIOR	--	--					
ALINEAMIENTO DE FACHADA	--	--					
Nº DE ESTACIONAMIENTO	--	--					
				AREA TECHADA			73.85 m2
				AREA LIBRE			453.55 m2
				AREA DEL TERRENO			527.40 m2

UBICACIÓN
Esc. 1/500

CONSTRUCORA MAZA QUIROZ E.I.R.L.
RUC / 2060732035
Daniel Antonio Maza Vasquez
TITULAR GERENTE

Betty Sofia Cueva Reátegui
INGENIERA CIVIL
CIP: 111425

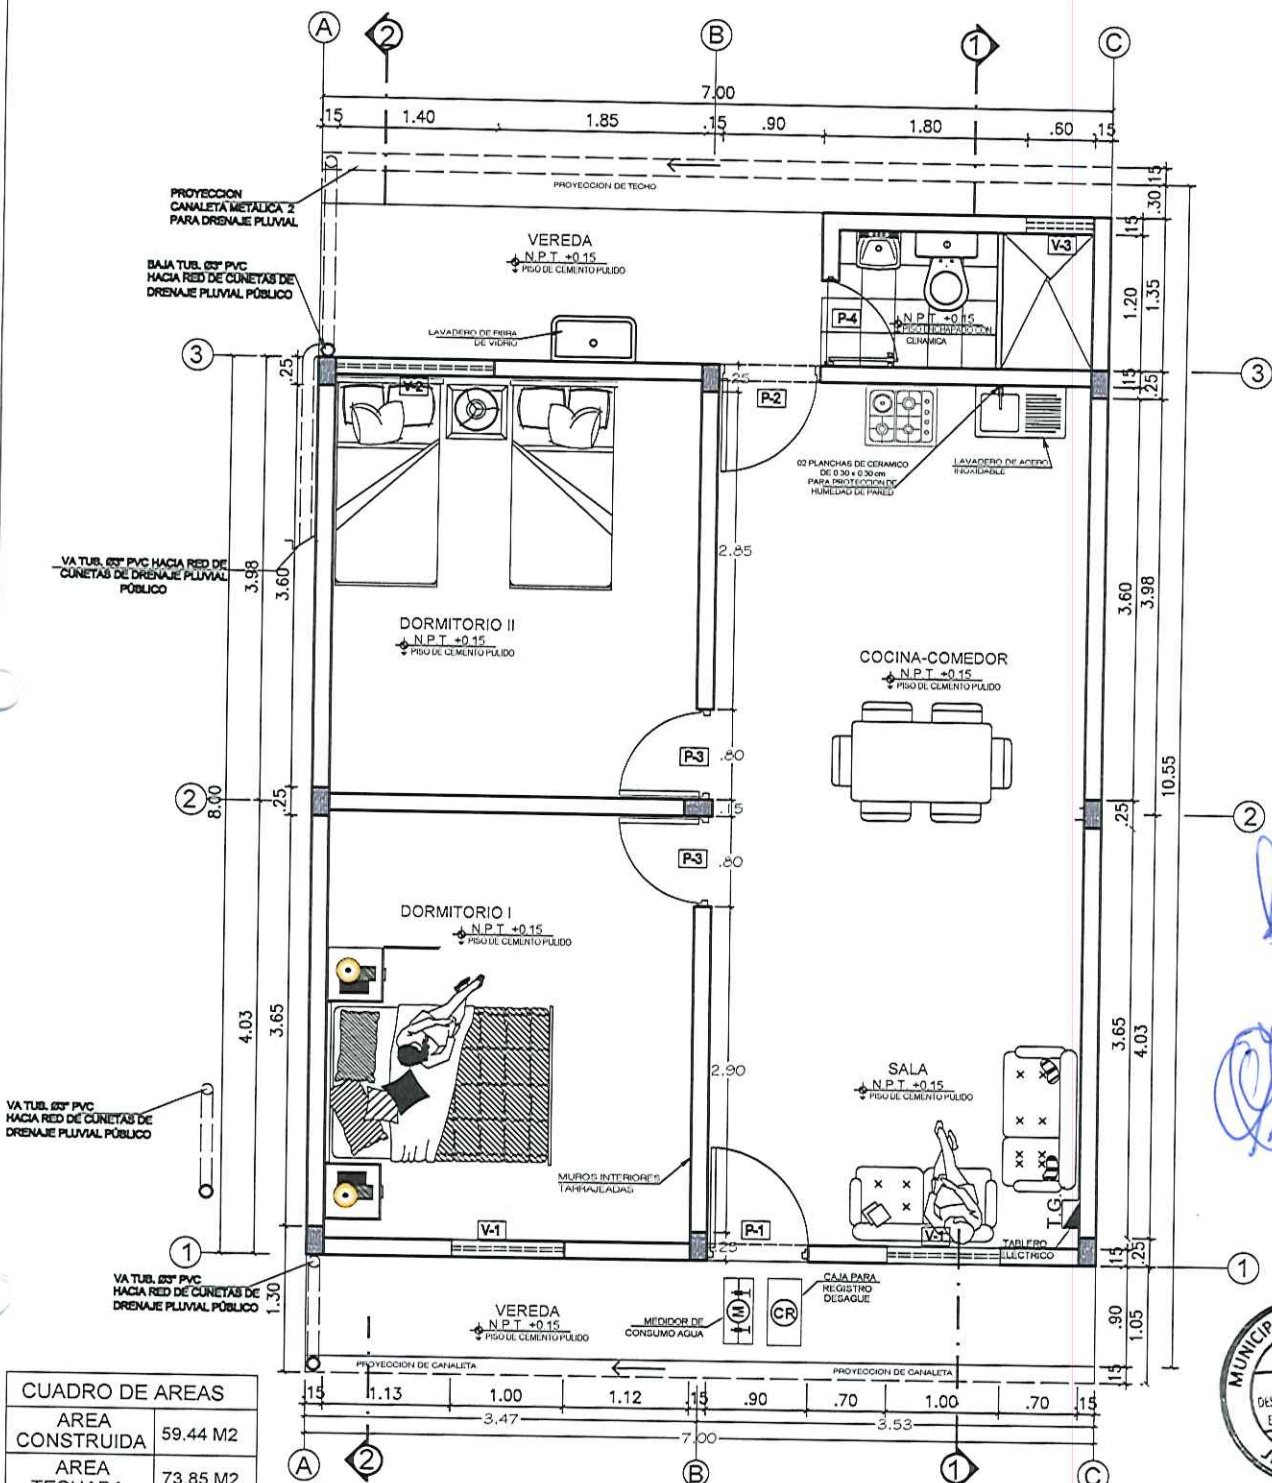

CUADRO DE AREAS	
AREA CONSTRUIDA	59.44 M2
AREA TECHADA	73.85 M2

ARQUITECTURA-DISTRIBUCION

ESC: 1/50

ESPECIFICACIONES TECNICAS	
PISOS	CEMENTO PULIDO EN AMBIENTES INTERIORES Y SEMIPULIDO EN AREA DE LAVANDERIA. EN BAÑOS: CERAMICA, INCLUIDO FONDO DE DUCHA Y SARDINEL


CUADRO DE VANOS					
VENTANAS					CARACTERISTICAS
TIPO	ANCHO	ALTO	ALFEIZAR	CANTIDAD	
V1	1.00	1.40	1.20	03	
V2	0.60	0.30	2.30	01	
PUERTAS					CARACTERISTICAS
TIPO	ANCHO	ALTO	SOBRE LUZ	CANTIDAD	
P1	0.90	2.10	0.50	01	
P2	0.90	2.10	0.50	01	
P3	0.80	2.10	0.50	02	
P4	0.75	2.10	0.50	01	

MINISTERIO DE VIVIENDA CONSTRUCCIÓN Y SANEAMIENTO		ENTIDAD RESPONSABLE: CONSTRUCTORA MAZA QUIROZ E.I.R.L	
PROYECTO: VIVIENDA DE INTERÉS SOCIAL - CONSTRUCCIÓN EN SITIO PROPIO			
PROPIETARIO: DANIEL SUAREZ CALDERON			
UBICACION: JR.MOYOBAMBA, LT. 5, MZ.2, BARRIO MIRAFLORES, DISTRITO JEPELACIO, PROVINCIA MOYOBAMBA, DPTO. SAN MARTIN			
PLANO: ARQUITECTURA - DISTRIBUCIÓN		FECHA: MARZO 2024	LAMINA N°: A-01
PROFESIONAL: ARQ. PATRICIA ESCOBAR ABRIL		ESCALA: 1/75	
CONSTRUCTORA MAZAQUIROZ E.I.R.L			

Bety Cueva Patategui
INGENIERA CIVIL
CIP: 111425

Patricia Escobar Abril
ARQUITECTA
N° Reg. C.A.P. 5259



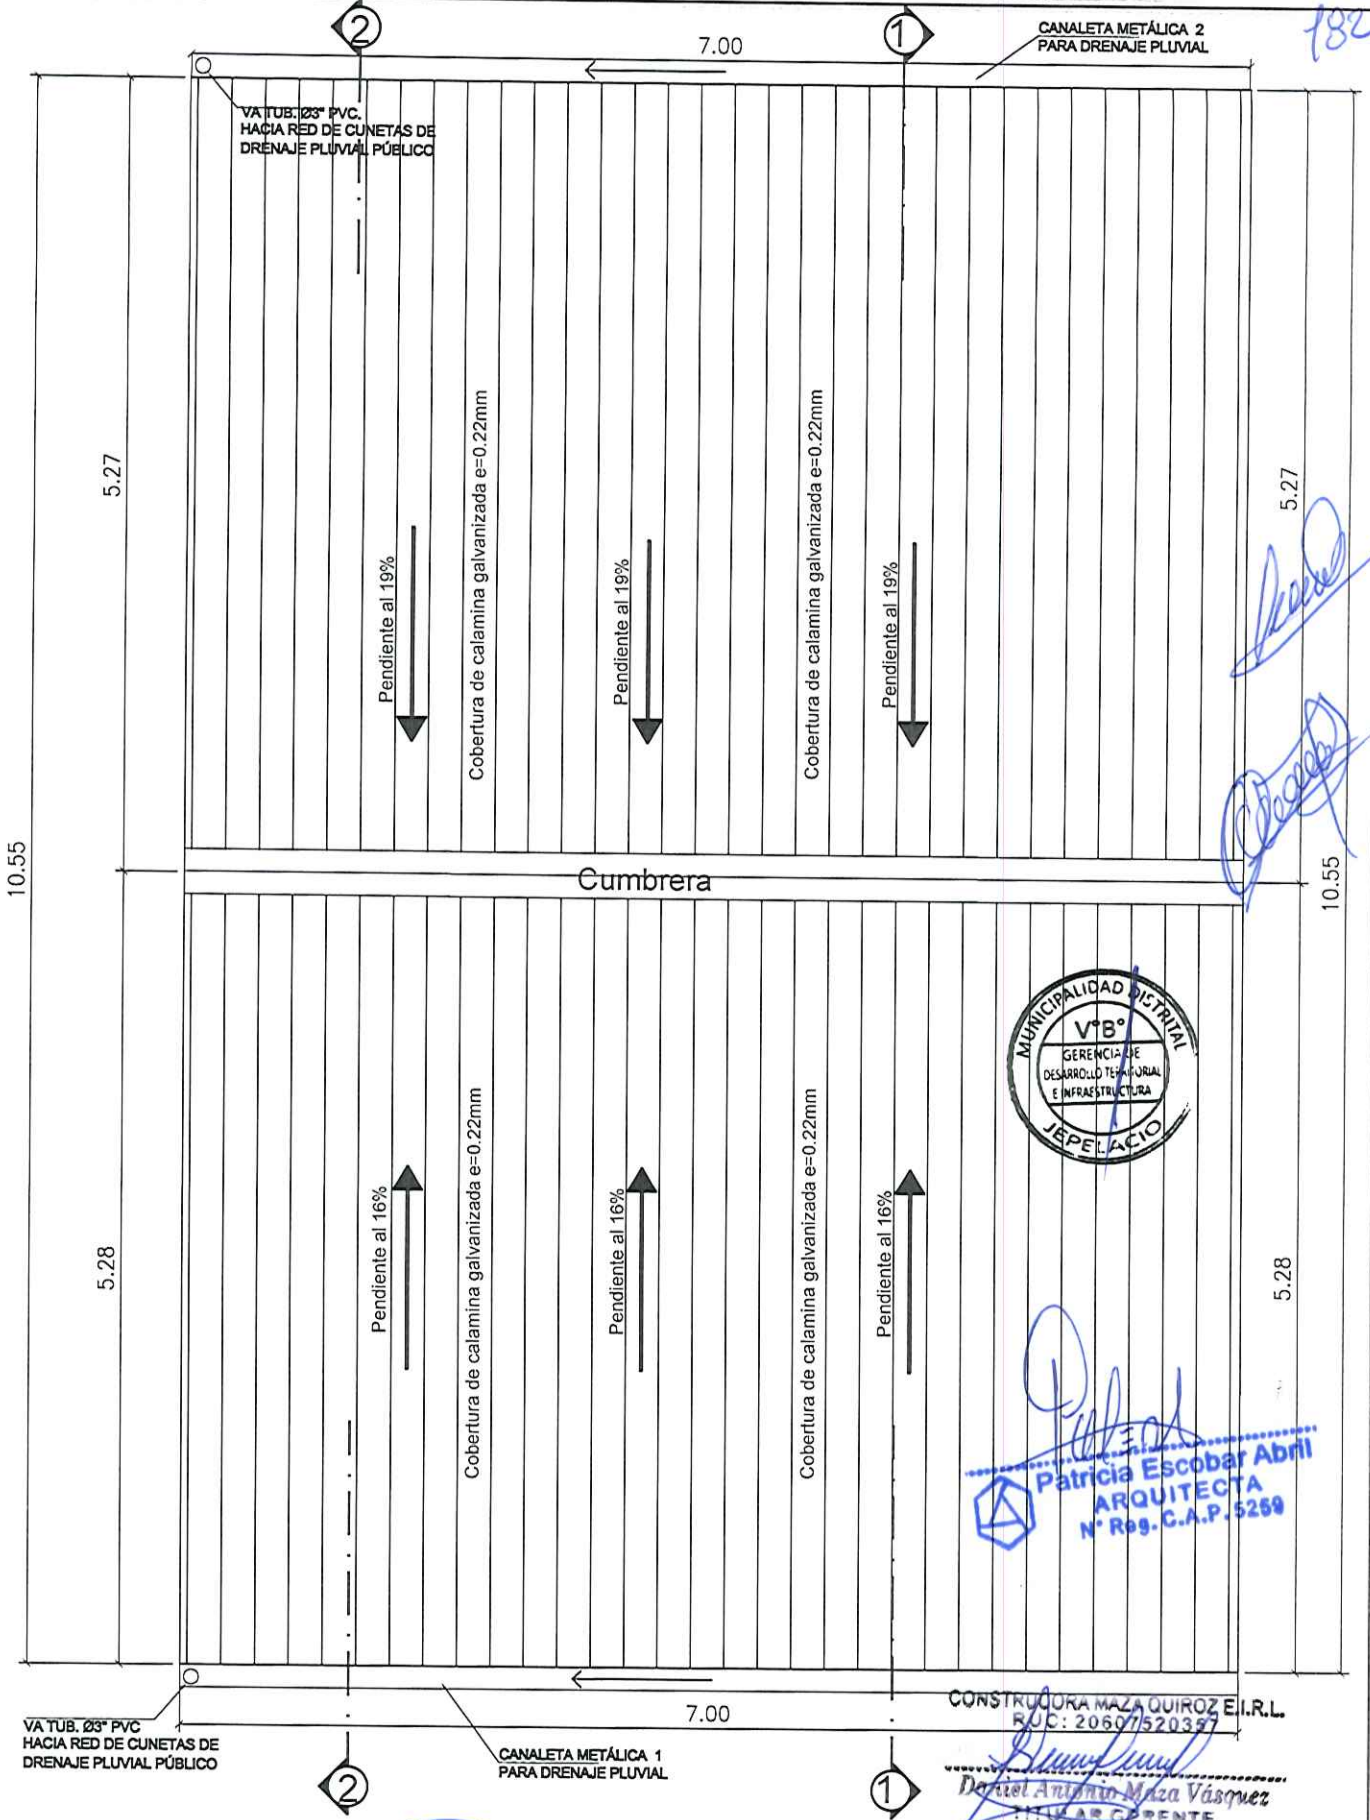

PLANO DE TECHOS

ESC: 1/50

Bety Sofia Cueva Reátegui
INGENIERA CIVIL
CIP: 111425


ESPECIFICACIONES TÉCNICAS

TECHO

ESTRUCTURA METÁLICA CON CORREAS DE 2"x1", CUBIERTA DE CALAMINA GALVANIZADA 0.20 mm. CON CANALETA PARA EVACUACIÓN PLUVIAL. (IMPERMEABILIZADO CON SISTEMA DE EVACUACIÓN DE AGUAS DE LLUVIA.)

MINISTERIO DE VIVIENDA CONSTRUCCIÓN Y SANEAMIENTO	ENTIDAD RESPONSABLE: CONSTRUCTORA MAZA QUIROZ E.I.R.L.
PROYECTO: VIVIENDA DE INTERÉS SOCIAL - CONSTRUCCIÓN EN SITIO PROPIO	
PROPIETARIO: DANIEL SUAREZ CALDERON	
UBICACIÓN: JR. MOYOBAMBA, LT.5, MZ.2, BARRIO MIRAFLORES, DISTRITO JEPELACIO, PROVINCIA MOYOBAMBA, DPTO. SAN MARTIN	
PLANO: ARQUITECTURA - TECHO LIVIANO	FECHA: MARZO 2024
PROFESIONAL: ARQ. PATRICIA ESCOBAR ABRIL	ESCALA: 1/50
	LAMINA N°: A-02

ESPECIFICACIONES TÉCNICAS	
TECHO	Estructura metálica con correas de 2" x 1.2", cubierta de calamina galvanizada 0.20 mm. Con canaletas para evacuación pluvial. (IMPERMEABILIZADO CON SISTEMA DE EVACUACIÓN DE AGUAS DE LLUVIA.)
PISO	Cemento pulido en ambientes interiores y semipulido en área de lavandería.
	En baños: Cerámica, incluido fondo de ducha y sordinel
	En fachada: tarrajeado y pintado color ocre con retoques de color gris. Muros interiores tarrajeado. Columnas y vigas interiores: tarrajeados y pintado. Cerámicos en servicios higiénicos: h=1.80m en ducha y 1.20m en pared detrás de los aparatos sanitarios. 02 planchas de cerámica de 0.30 x 0.30 cm, sobre lavadero de ropa y cocina.

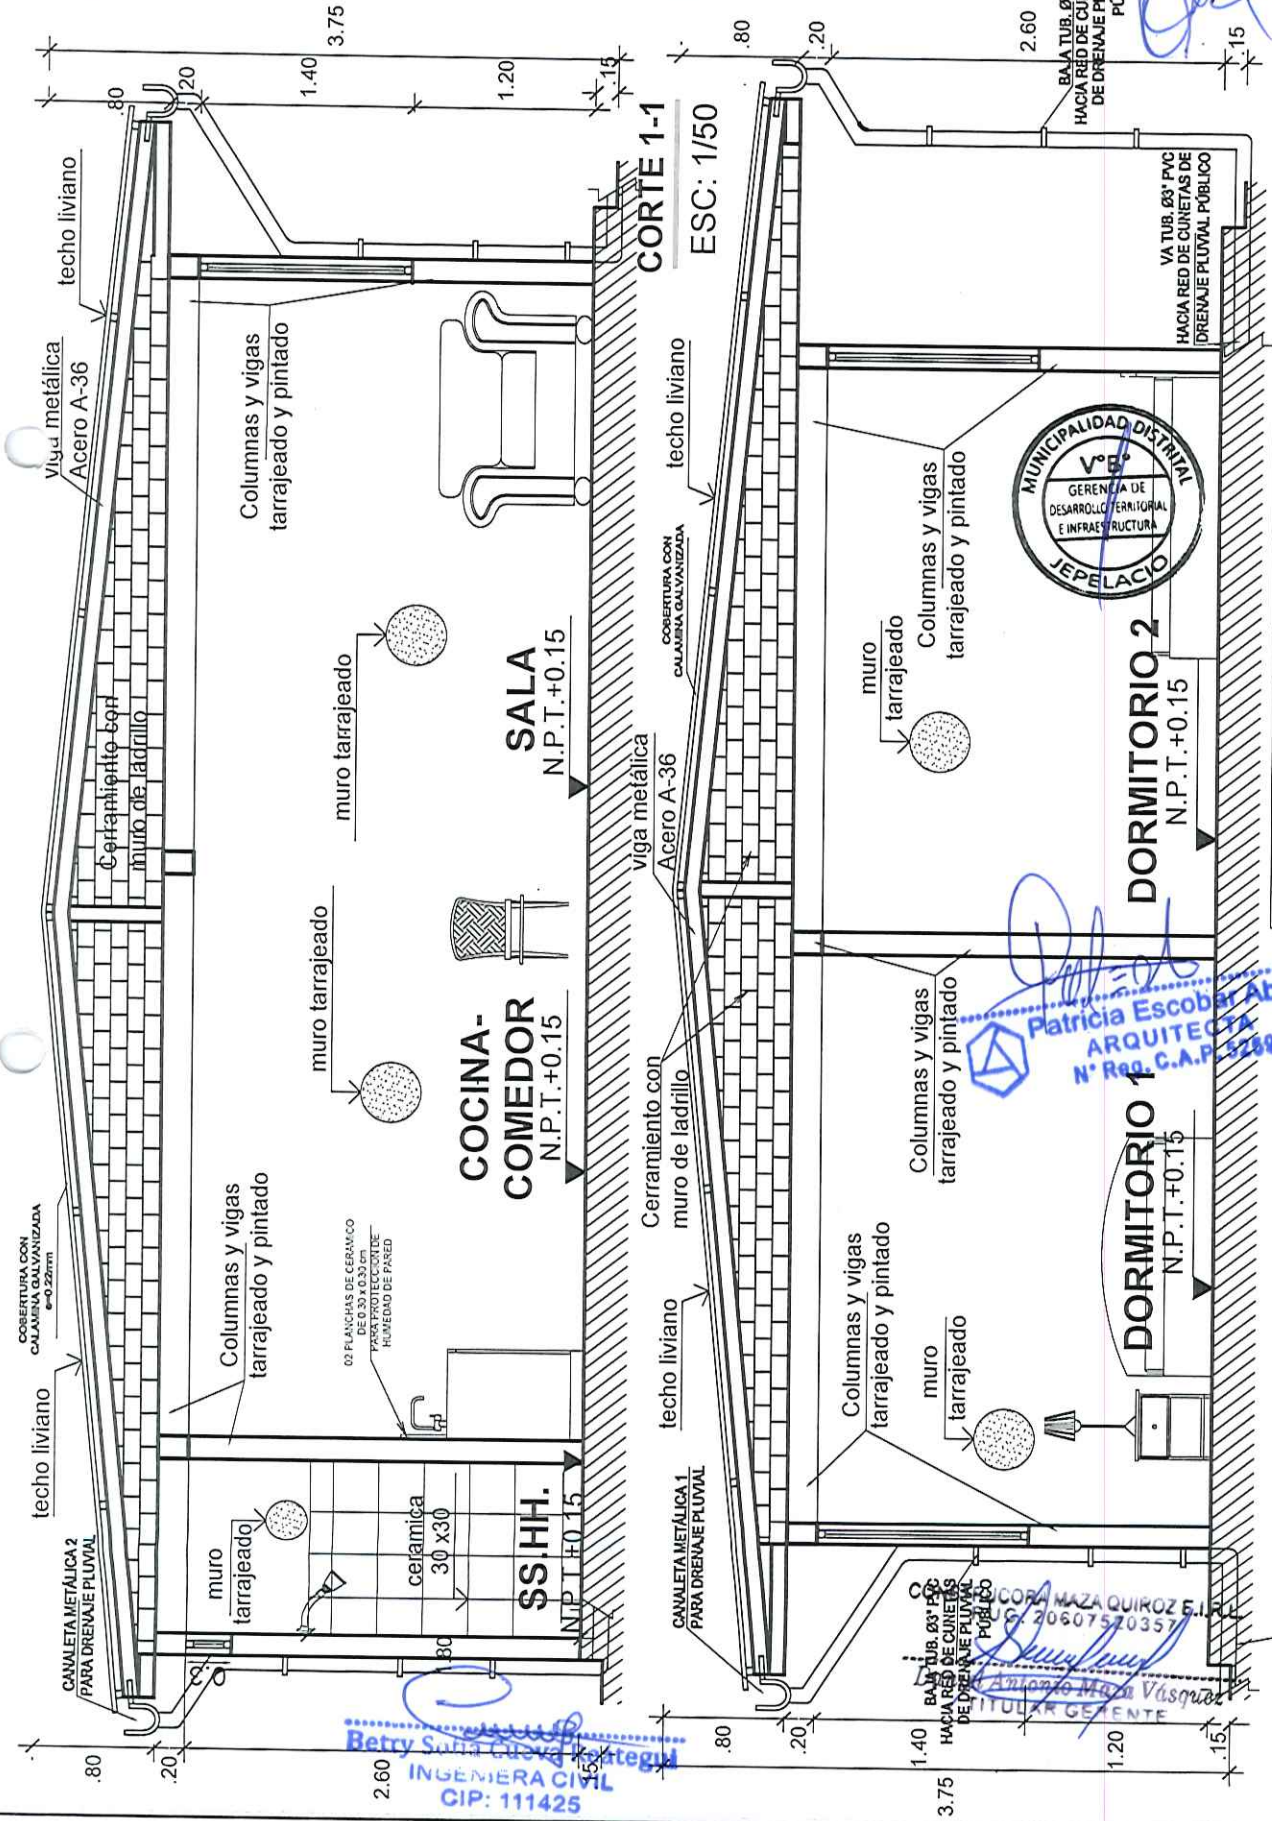

PROPIETARIO:	DANIEL SUAREZ CALDERON
UBICACION:	JR. MOYOBAMBA, LT. 5, MZ. 2, BARRIO MIRAFLORES, DISTRITO JEPELACIO, PROVINCIA MOYOBAMBA, DPTO. SAN MARTIN
PLANO:	ARQUITECTURA - CORTES
FECHA:	MARZO 2024
ESCALA:	1/50
LAMINA N°:	A-03

MINISTERIO DE VIVIENDA CONSTRUCCION Y SANEAMIENTO	ENTIDAD RESPONSABLE: CONSTRUCTORA MAZA QUIROZ EIRL
PROYECTO: VIVIENDA DE INTERES SOCIAL - CONSTRUCCION EN SITIO PROPIO	

ESPECIFICACIONES TÉCNICAS
- LA OBRA CONSISTE EN LA CONSTRUCCION DE VIVIENDAS DEL TIPO ECONOMICAS SIN POSIBILIDAD AL CRECIMIENTO VERTICAL, MAS SI HORIZONTAL. EL SISTEMA CONTEMPLA UN AMBIENTE MULTI USO PARA (SALA, COMEDOR, COCINA), 01 SERVICIO HIGIENICO, 01 LAVANDERIA, Y 02 DORMITORIOS.

CORTE 2-2	
ESC: 1/50	




Patricia Escobar Abrial
ARQUITECTA
Nº Reg. C.A.P. 5289

Betty Soria Cueva
INGENIERA CIVIL
CIP: 111425


CONSTR. MAZA QUIROZ E.I.R.L.
RUC: 20607570351
Antonio Maza Vásquez
TITULAR GERENTE

ESPECIFICACIONES TECNICAS	
CARPINTERIA	Puerta principal y posterior: Metálica de plancha galvanizada acanalada e=1.24mm Puerta interiores: Contraplacada e=4cm y marco de madera. Bisagras copuchinas. Ventanas: Con marco de aluminio y hojas con vidrio de 6mm con marco en sus cuatro lados.
CERRAJERIA	2 Golpes en puerta principal y tipo perfil en puertas interiores
APARATOS SANITARIOS Y GRIFERIA	SERVICIOS HIGIENICOS: 1 Inodoro y 1 lavatorio de losa nacional. COCINA: Lavadero de acero inoxidable 01 poza con escurridero y grifería cromada metálica, con 02 cerámicos de 0.30x0.30 cm para protección de humedad. EXTERIOR: 1 lavadero de fibra de vidrio y grifería metálica. Grifería cromada metálica en aparatos sanitarios con sistema reductor de caudal, con 02 cerámicos de 0.30x0.30 cm para protección de humedad.

ESPECIFICACIONES TECNICAS	
INSTALACIONES ELÉCTRICAS	Tablero General con 3 llaves termomagnéticas y un interruptor diferencial, tubería PVC SAP pasado, tubería empotrada, placas en tomacorrientes e interruptores de baquelita y wall sockets en salida de luz con artefacto, instalación de timbre
INSTALACIONES SANITARIAS	Red de desagüe de tubería PVC SAL con caja de registro que evacuará a la red pública. Red de agua tubería PVC SAP, roscada, montante 4" para desagüe, proyección 2do piso como parte del sistema desagüe.

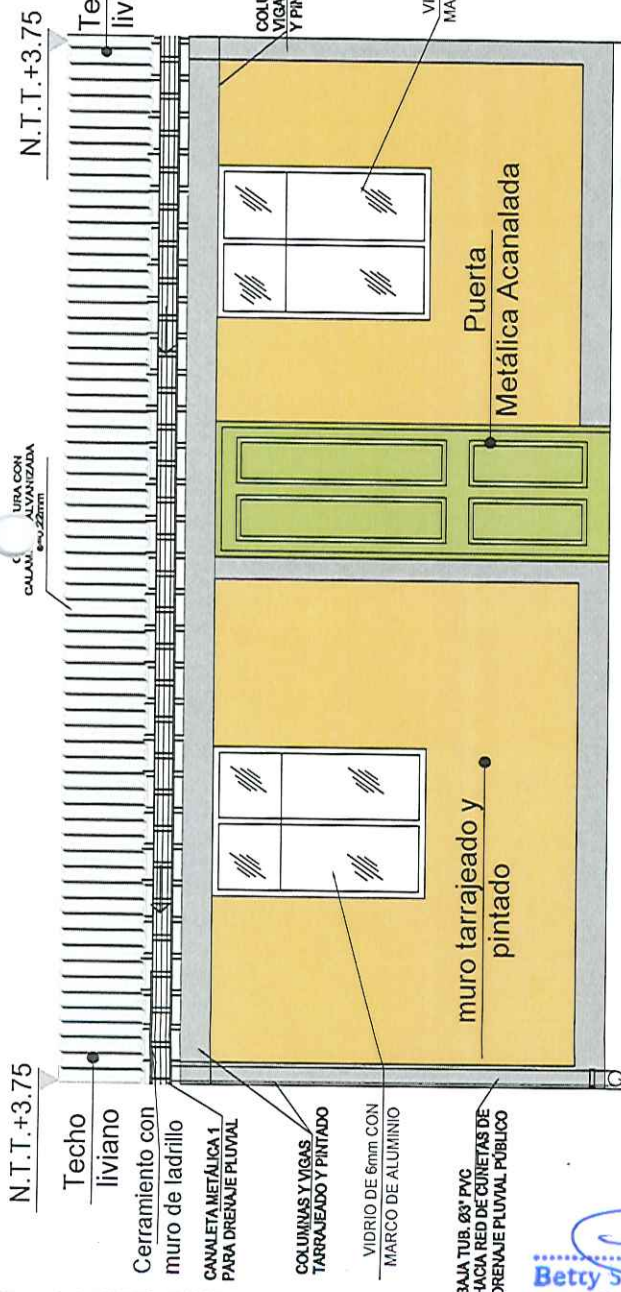

ELEVACIÓN PRINCIPAL
ESCALA: 1/50

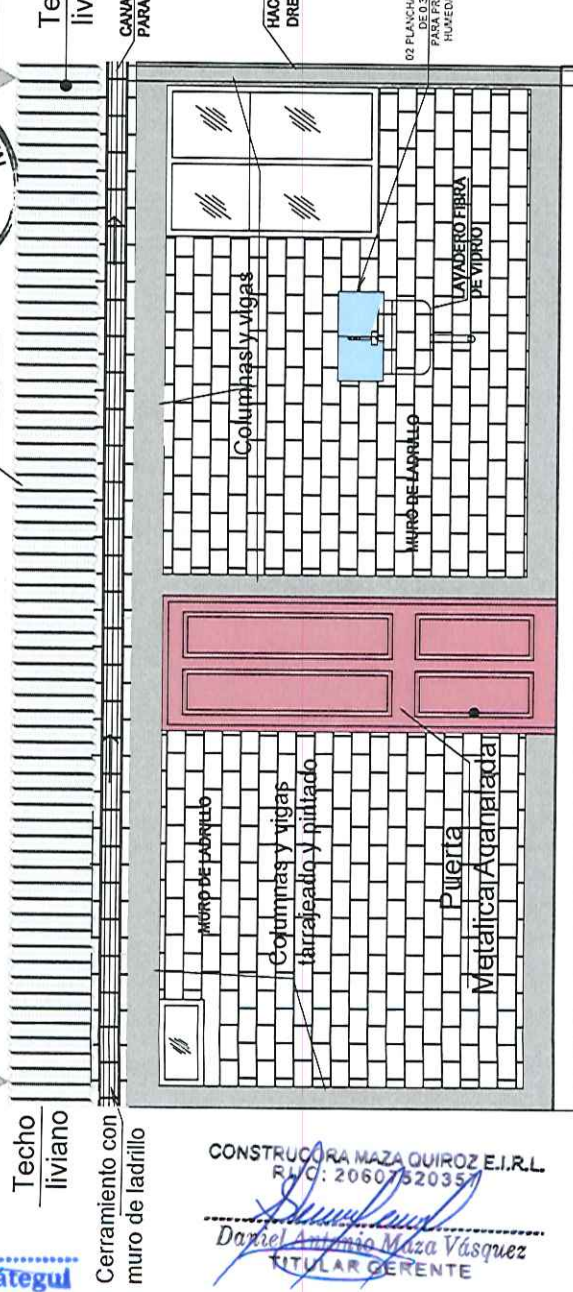

ELEVACIÓN POSTERIOR
ESCALA: 1/50

Patricia Escobar Abril
ARQUITECTA
N° Reg. C.A.P. 5259

MINISTERIO DE VIVIENDA CONSTRUCCIÓN Y SANEAMIENTO	ENTIDAD RESPONSABLE: CONSTRUCTORA MAZA QUIROZ EIRL
PROYECTO: VIVIENDA DE INTERÉS SOCIAL - CONSTRUCCIÓN EN SITIO PROPIO	PROPIETARIO: DANIEL SUAREZ CALDERON
UBICACIÓN: JR. MOYOBAMBA, LT 5, MZ 2, BARRIO MIRAFLORES, DISTRITO JEPELACIO, PROVINCIA MOYOBAMBA, DPTO. SAN MARTIN	PLANO: ARQUITECTURA - CORTE Y ELEVACION
FECHA: MARZO 2024	LAMINA N°: A-04
ESCALA: 1/50	ARQ. PATRICIA ESCOBAR ABRIL

CONSTRUCTORA MAZA QUIROZ E.I.R.L.
R.N.C: 2060752035
Daniel Antonio Maza Vásquez
TITULAR GERENTE

Betty Soria Cueva Reátegui
INGENIERA CIVIL
CIP: 111425

BAJA TUB. Ø4" PVC
DRENAJE PLUVIAL
HACIA SISTEMA DE
DRENAJE PÚBLICO

TECHO
METÁLICO
LIVIANO

DETALLE DE DRENAJE PLUVIAL

CANAleta Ø4"

TECHO
METÁLICO
LIVIANO

PROYECCIÓN TUBO Ø4"
SISTEMA DE SALIDA
PLUVIAL

DETALLE PLUVIAL EN TECHO METÁLICO

TECHO
METÁLICO
LIVIANO

canaleta metálica
para drenaje
pluvial

BAJA TUBO
PVC Ø4"

PROYECCIÓN
VEREDA

BAJA TUB. Ø4" PVC
DRENAJE PLUVIAL
HACIA CUNETA PARA
DRENAJE PLUVIAL
PÚBLICO

CUNETA PÚBLICA DE DRENAJE
PLUVIAL

PLANO DE DRENAJE PLUVIAL

ESC: 1/50

ESPECIFICACIONES TÉCNICAS

DRENAJE PLUVIAL DESEMBOCA A CUNETA DE DRENAJE PLUVIAL PÚBLICO

CONSTRUCTORA MAZA QUIROZ E.I.R.L.
RUC: 20601520357

Daniel Antonio Maza Vásquez
TITULAR GERENTE

Betty Sofia Cueva Reátegui

MINISTERIO DE VIVIENDA CONSTRUCCIÓN Y SANEAMIENTO		ENTIDAD RESPONSABLE: CONSTRUCTORA MAZA QUIROZ E.I.R.L.
PROYECTO: VIVIENDA DE INTERÉS SOCIAL - CONSTRUCCIÓN EN SITIO PROPIO		
PROPIETARIO: DANIEL SUAREZ CALDERON		
UBICACIÓN: JR.MOYOBAMBA, LT.5, MZ.2, BARRIO MIRAFLORES, DISTRITO JEPELACIO, PROVINCIA MOYOBAMBA, DPTO. SAN MARTIN		
PLANO: DRENAJE PLUVIAL	FECHA: MARZO 2024	LAMINA N°: A-05
PROFESIONAL: ARQ. PATRICIA ESCOBAR ABRIL	ESCALA: 1 / 50	